




SECTION K4-K4
(SCALE 1:40)

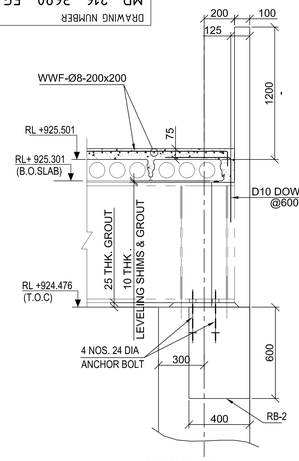


SECTION A-A
(SCALE 1:20)

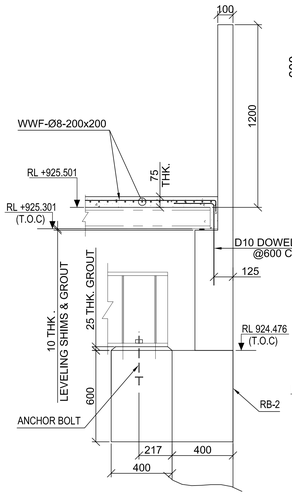


SECTION B-B
(SCALE 1:20)

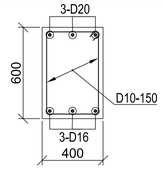


SECTION C-C
(SCALE 1:20)

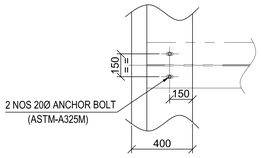


DETAIL MKD. 'C'
(SCALE 1:20)

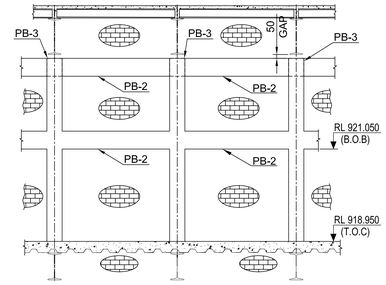


SECTION K3-K3
(SCALE 1:40)

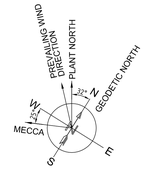


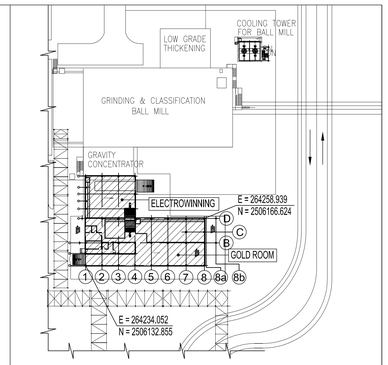


KEY PLAN
SCALE 1:1000

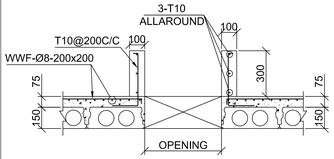


TYPICAL DETAIL OF OPENING
(SCALE 1:20)

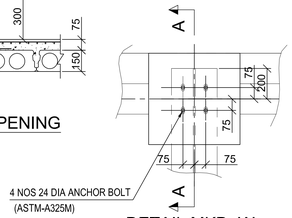


DETAIL MKD. 'A'
(SCALE 1:20)

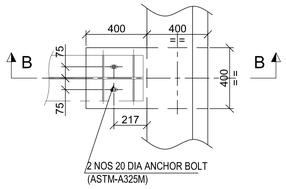


DETAIL MKD. 'B'
(SCALE 1:20)

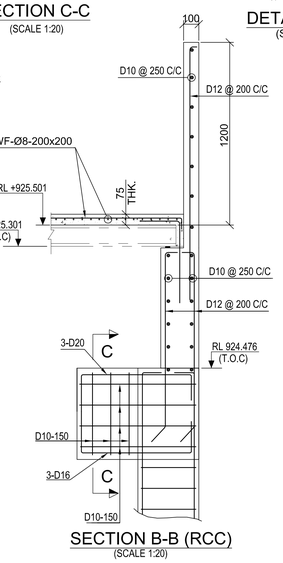

SECTION B-B (RCC)
(SCALE 1:20)

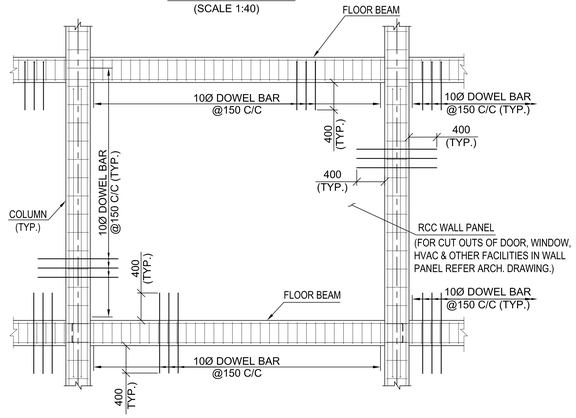


TYP. DETAIL OF RC WALL PANEL SHOWING DOWEL BARS
SCALE 1:50

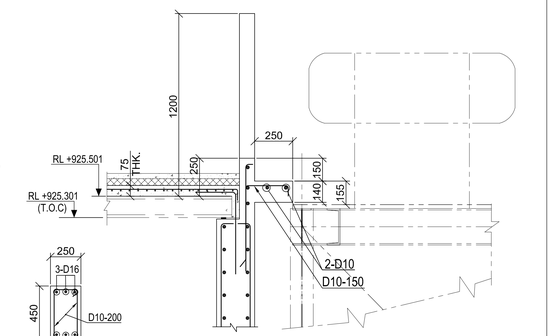


SECTION S-S
(SCALE 1:20)


TYP. SECTION
OF PB-2 & PB-3
SCALE 1:25
(RC DETAILS)

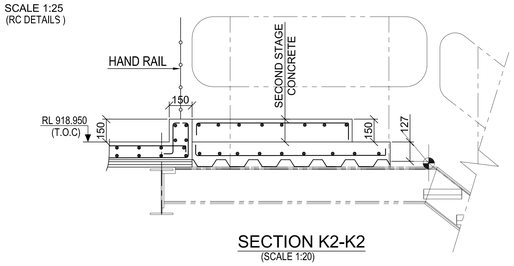


SECTION K2-K2
(SCALE 1:20)

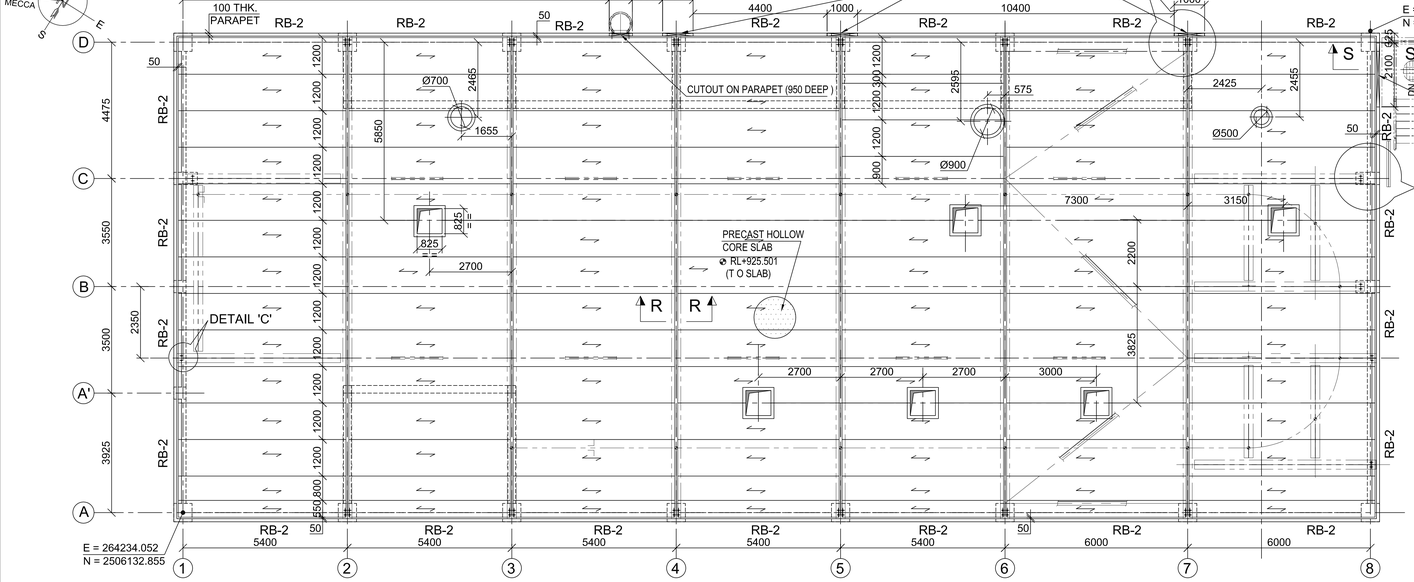


PLAN AT RL +925.501 M LEVEL
SPAN OF HOLLOW CORE SLAB MKD. THUS
(SCALE - 1:100)

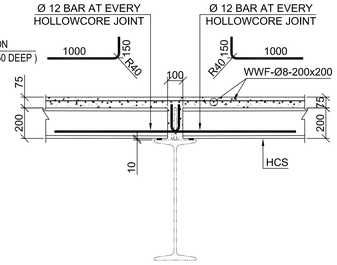

SECTION R-R
(SCALE 1:20)

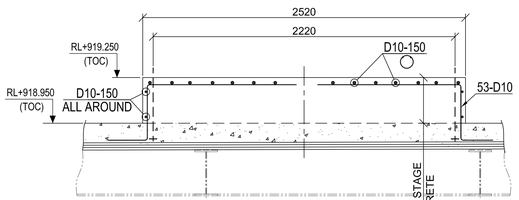

SECTION K-K
(SCALE 1:20)

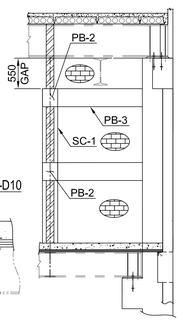

SECTION K5-K5
(SCALE 1:40)

LEGEND :-

R.L. - REDUCED LEVEL
T.O.C. - TOP OF CONCRETE.
TYP. - TYPICAL.
MKD. - MARKED.
B/W - BOTH WAY
THK - THICK
T O SLAB - TOP OF SLAB
DIA - DIAMETER
RCC - REINFORCED CEMENT CONCRETE

NOTES:-

1. ALL DIMENSIONS ARE IN MILLIMETRES AND LEVELS AND CO-ORDINATES ARE IN METRES UNLESS OTHERWISE STATED.
2. GRADE OF CONCRETE SHALL BE 35 MPa FOR FOUNDATION, 30 MPa FOR GRADE SLAB & 15 MPa FOR BLINDING CONCRETE.
3. GRADE OF REINFORCEMENT SHALL BE DEFORMED BAR 420 MPa (GRADE 60) - ASTM A615/A615M.
4. THIS DRAWING SHOULD BE READ WITH DRAWING NO. MD-216-3690-EG-CV-GAD-1357,1358,1359,1360,1361 MD-216-3690-EG-CV-DED-1364,1365,1367,1368

DOCUMENT NUMBER	REFERENCE DOCUMENTS	REV	DATE	REVISION DESCRIPTION	DRN	CHK	ENG	APP	EMP
		D01	13/10/2023	AS - BUILT	AUD	SJM	SNM	PRI	
MD-216-3690-EG-ST-GAD-1002	PLAN AT +925.251, SECTION A-A, B-B AND C-C	C03	12/03/2021	ISSUED FOR CONSTRUCTION & REVISED AS MARKED C03	AUD	SJM	SNM	PRI	
MD-216-3690-EG-ST-GAD-1001	PLAN AT +925.251, SECTION A-A - E-E	C02	09/01/2021	ISSUED FOR CONSTRUCTION & REVISED AS MARKED C02	AUD	SJM	SNM	PRI	
MD-216-3690-EG-CV-GAD-1002	PLAN AT EL. +913.100 GOLD ROOM AND ELECTROWINNING	C01	01/06/2020	ISSUED FOR CONSTRUCTION & REVISED AS MARKED	AUD	SJM	SNM	PRI	
MD-216-3690-EG-CV-GAD-1001	PLAN AT EL. +913.100 GOLD ROOM AND ELECTROWINNING	A01	30/05/2020	ISSUED FOR REFERENCE	AUD	SJM	SNM	PRI	

RESERVED FOR VENDOR LOGO AND DRAWING NUMBER

LARSEN & TOUBRO

This drawing is the property of *LARSEN & TOUBRO* and must not be passed on to any person or body not authorized by us to receive it nor be copied or otherwise made use either in full or in part by such person or body without our prior permission in writing.

Outotec

The content of these documents are the sole property of Outotec Oyj. Any rights not expressly granted herein are reserved. Reproduction, transfer or distribution of part or all of the contents in any form without prior written permission of Outotec is prohibited.

MA'ADEN معادن
Saudi Arabian Mining Company شركة معادن العربية السعودية

This document and the information contained herein is Ma'aden proprietary know-how. This document or any part thereof should not be reproduced, stored in a retrieval system or transmitted by any means, electronic or otherwise, or divulged without prior written permission of Ma'aden.

LARSEN & TOUBRO DRAWING NUMBER: 019045_450_C_D_24146_003 — REVISION: 4
OUTOTEC DRAWING NUMBER: 900707 _GAU01 _EE14 _CTB17 _36903 — DOCUMENT ID: OU100684635 — REVISION: 4

DRAWN	AUD	20/05/2020
CHECKED	SJM	25/05/2020
ENGINEER	SNM	10/05/2020
APPROVED	PRI	27/05/2020
EMPLOYER		
SCALE	1:100	A1

MANSOURAH - MASSARAH GOLD PROJECT
DETAIL DRAWING
GOLD ROOM
GA & DETAIL OF PLAN AT +925.451 M LEVEL

DRAWING NUMBER: MD - 216 - 3690 - EG - CV - DED -1366 — REV: D01