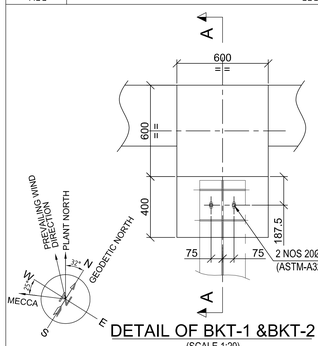
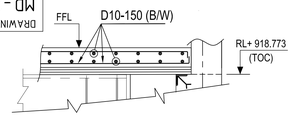
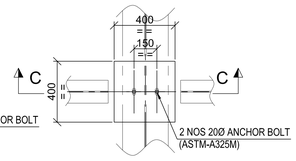
DRAWING NUMBER MD-216-3690-EG-CV-GAD-1359 REV D01



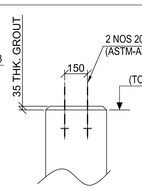

DETAIL OF BKT-1 &BKT-2
(SCALE 1:20)



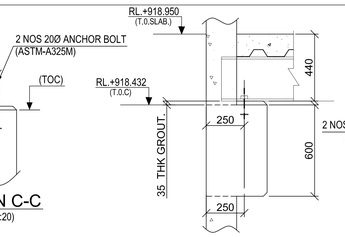

TYP. RCC DETAIL OF DECK SLAB
(SCALE 1:20)



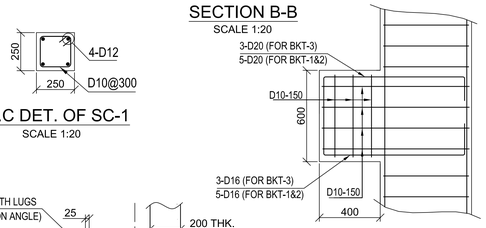

DETAIL MKD. 'C'
(SCALE 1:20)



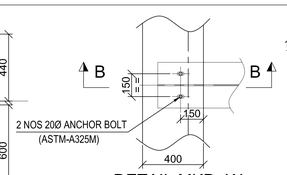

SECTION C-C
(SCALE 1:20)



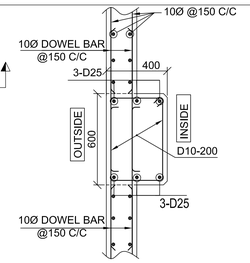

SECTION B-B
SCALE 1:20



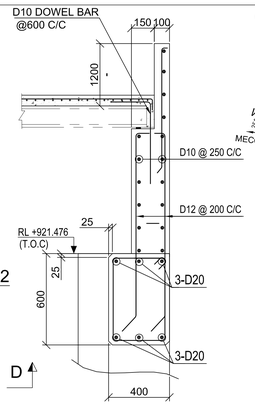

RCC DETAIL OF
BKT 1, BKT-2 , BKT-3
(SCALE 1:20)



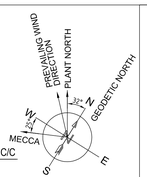

DETAIL MKD. 'A'
(SCALE 1:20)

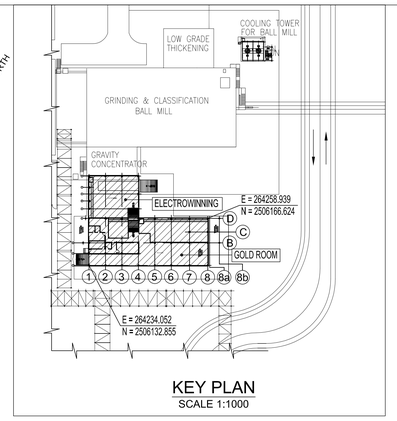



R.C DETAILS FOR BEAM MKD B2
SCALE 1:20




SECTION F-F
SHOWING R.C.C
(SCALE 1:20)




KEY PLAN
SCALE 1:1000




R.C DET. OF SC-1
SCALE 1:20



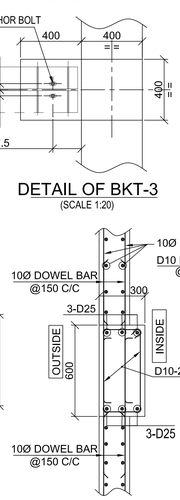

SECTION A-A
(SCALE 1:20)




SECTION K1-K1
(RCC DETAILS)
(SCALE 1:20)



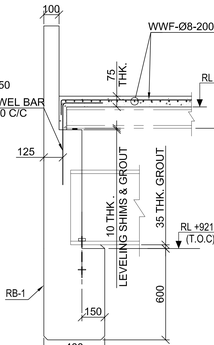

SECTION D-D
(SCALE 1:20)



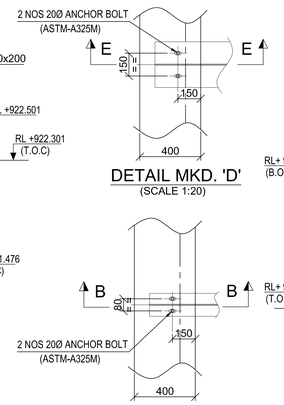

DETAIL OF BKT-3
(SCALE 1:20)




R.C DETAILS FOR
BEAM MKD B1
SCALE 1:20

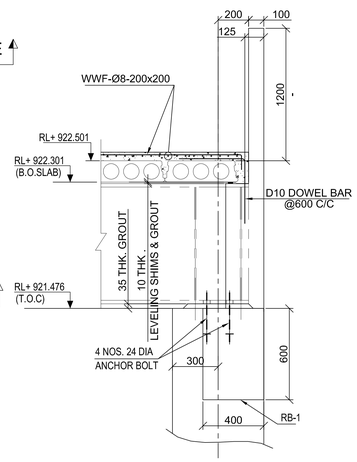



SECTION E-E
SCALE 1:20

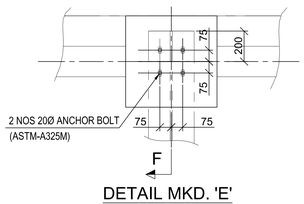



DETAIL MKD. 'D'
(SCALE 1:20)

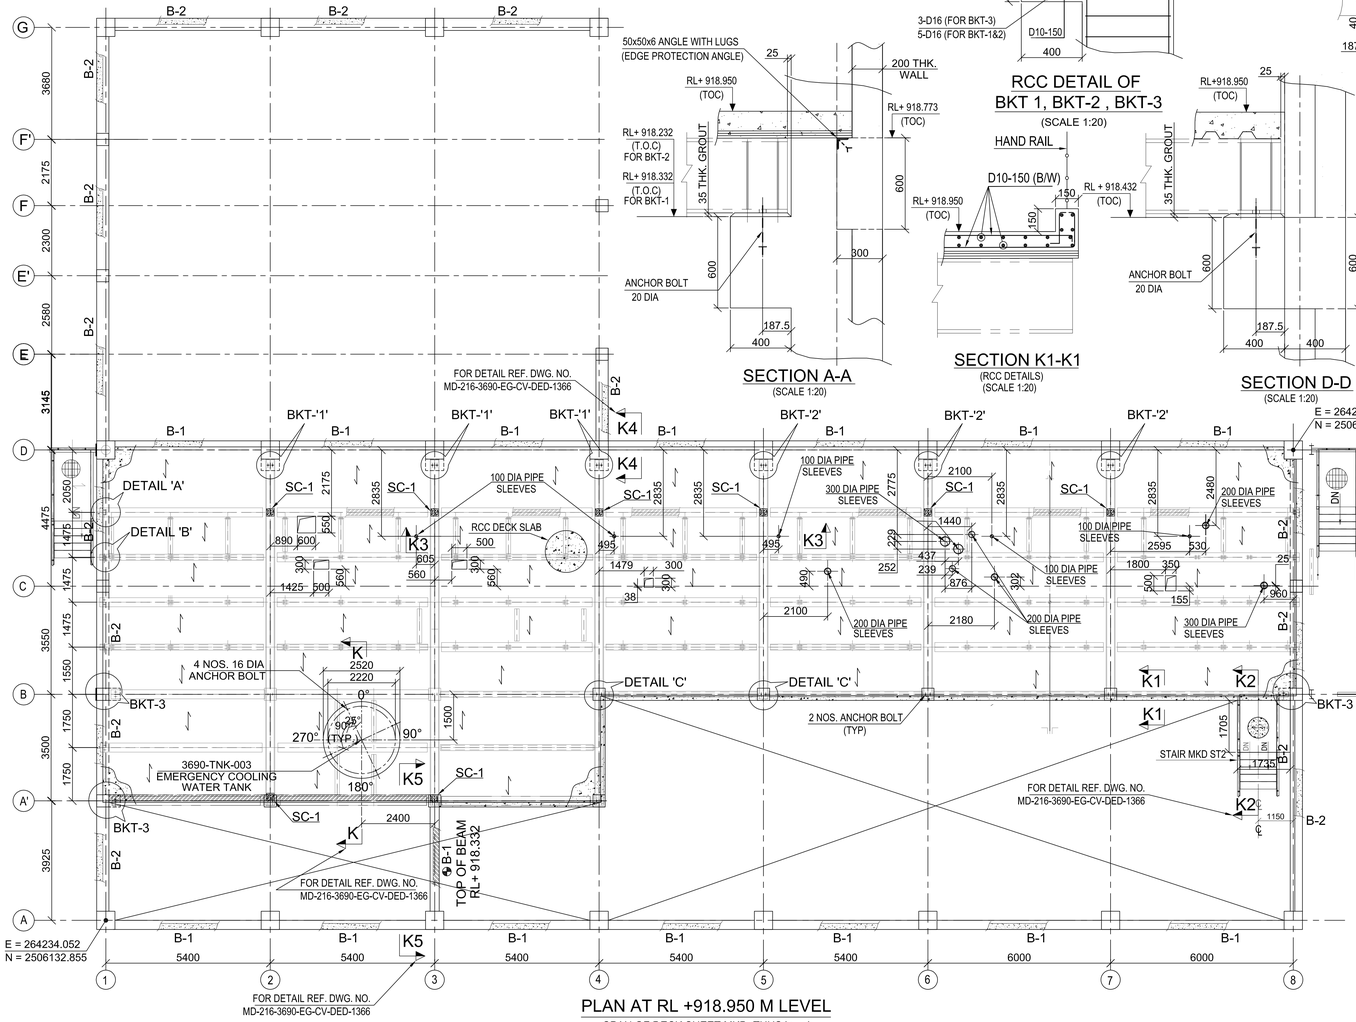
DETAIL MKD. 'B'
(SCALE 1:20)



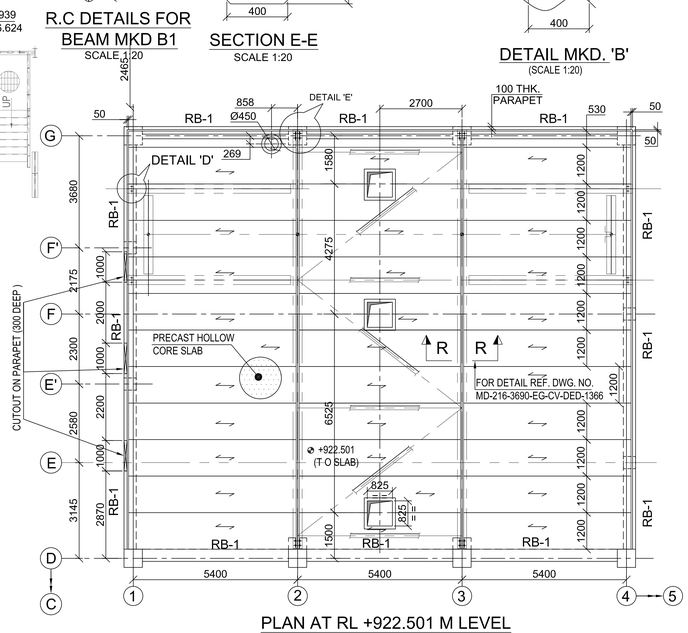

SECTION F-F
(SCALE 1:20)




DETAIL MKD. 'E'
(SCALE 1:20)




PLAN AT RL +918.950 M LEVEL
SPAN OF DECK SHEET MKD. THUS '⟷'
TOP OF BEAM MKD. 'B1' AT RL +918.773 & TOP OF BEAM MKD. 'B2' AT RL +918.432
(SCALE - 1:100)




PLAN AT RL +922.501 M LEVEL
SPAN OF HOLLOW CORE SLAB MKD. THUS '⟷'
(SCALE - 1:100)

LEGEND :-
R.L. - REDUCED LEVEL
T.O.C. - TOP OF CONCRETE.
TYP. - TYPICAL.
R.C.C - REINFORCED CEMENT CONCRETE
MKD. - MARKED.
B/W - BOTH WAY
THK - THICK
FFL - FINISHED FLOOR LEVEL

NOTES:-
1. GRADE OF CONCRETE SHALL BE 35 MPa FOR RCC, 15 MPa FOR BLINDING CONCRETE.
2. GRADE OF REINFORCEMENT SHALL BE DEFORMED BAR 420 MPa (GRADE 60) - ASTM A615/A615M.
3. CLEAR COVER TO MAIN REINFORCEMENT SHALL BE SLAB - 15 MM., BEAM - 25 MM.
4. THIS DRAWING SHOULD BE READ WITH DRAWING NO. MD-216-3690-EG-CV-GAD-1357,1358,1360,1361 MD-216-3690-EG-CV-DED-1364,1365,1366,1367,1368

| DOCUMENT NUMBER | REFERENCE DOCUMENTS | REV | DATE | REVISION DESCRIPTION | DRN | CHK | ENG | APP | EMP |
|---|---|---|---|---|---|---|---|---|---|
| | | D01 | 13/10/2023 | AS - BUILT | AUD | SJM | SNM | PRI | |
| MD-216-3690-EG-ST-GAD-1002 | PLAN AT +925.251, SECTION A-A, B-B AND C-C | C03 | 12/03/2021 | ISSUED FOR CONSTRUCTION & REVISED AS MARKED C03 | AUD | SJM | SNM | PRI | |
| MD-216-3690-EG-ST-GAD-1001 | PLAN AT +925.251, SECTION A-A - E-E | C02 | 09/01/2021 | ISSUED FOR CONSTRUCTION & REVISED AS MARKED C02 | AUD | SJM | SNM | PRI | |
| MD-216-3690-EG-CV-GAD-1002 | PLAN AT EL. +913.100 GOLD ROOM AND ELECTROWINNING | C01 | 07/06/2020 | ISSUED FOR CONSTRUCTION & REVISED AS MARKED | AUD | SJM | SNM | PRI | |
| MD-216-3690-EG-CV-GAD-1001 | PLAN AT EL. +913.100 GOLD ROOM AND ELECTROWINNING | A01 | 30/05/2020 | ISSUED FOR REFERENCE | AUD | SJM | SNM | PRI | |

RESERVED FOR VENDOR LOGO AND DRAWING NUMBER

LARSEN & TOUBRO DRAWING NUMBER: 019045_450_C_G_24145_003 — REVISION: 4
OUTOTEC DRAWING NUMBER: 900707__GAU01__EE14__MTL01__36916 — DOCUMENT ID: OU100684644 — REVISION: 4

LARSEN & TOUBRO
This drawing is the property of LARSEN & TOUBRO and must not be passed on to any person or body not authorized by us to receive it nor be copied or otherwise made use either in full or in part by such person or body without our prior permission in writing.

Outotec
The content of these documents are the sole property of Outotec Oyj. Any rights not expressly granted herein are reserved. Reproduction, transfer or distribution of part or all of the contents in any form without prior written permission of Outotec is prohibited.

MA'ADEN معادن
Saudi Arabian Mining Company شركة معادن العربية السعودية
This document and the information contained herein is Ma'aden proprietary know-how. This document or any part thereof should not be reproduced, stored in a retrieval system or transmitted by any means, electronic or otherwise, or divulged without prior written permission of Ma'aden.

| | | | |
|---|---|---|---|
| DRAWN | AUD | 20/05/2020 | MANSOURAH - MASSARAH GOLD PROJECT |
| CHECKED | SJM | 25/05/2020 | GENERAL ARRANGEMENT DRAWING |
| ENGINEER | SNM | 10/05/2020 | GOLD ROOM |
| APPROVED | PRI | 27/05/2020 | GA & DETAIL PLAN AT +918.950 & +922.451 M LEVEL |
| EMPLOYER | | | |
| SCALE 1:100 | A1 | | DRAWING NUMBER: MD - 216 - 3690 - EG - CV - GAD-1359 — REV: D01 |