


DRAWING NUMBER: MD-216-3690-EG-CV-GAD-1360 REV D01

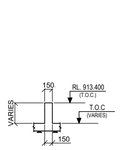


SECTION : G-G
SCALE 1:40

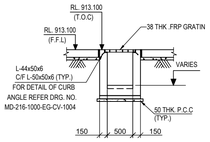


SECTION B1-B1
SCALE 1:40

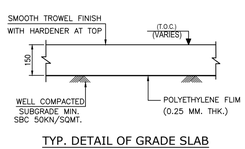


TYP. DETAIL OF GRADE SLAB
(FLOOR LOAD 15KN/SQM. TO 50KN/SQM.)
SCALE-1:10

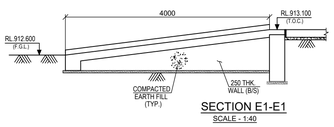


SECTION E1-E1
SCALE - 1:40

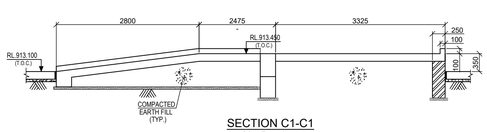


SECTION C1-C1
SCALE - 1:40

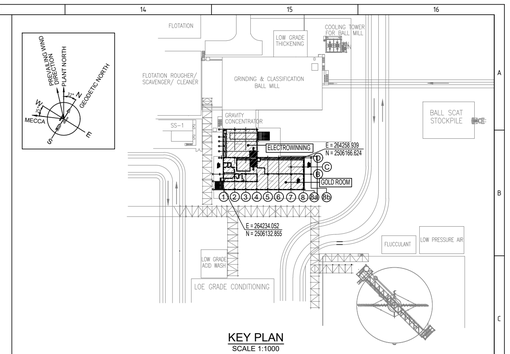


KEY PLAN
SCALE 1:1000

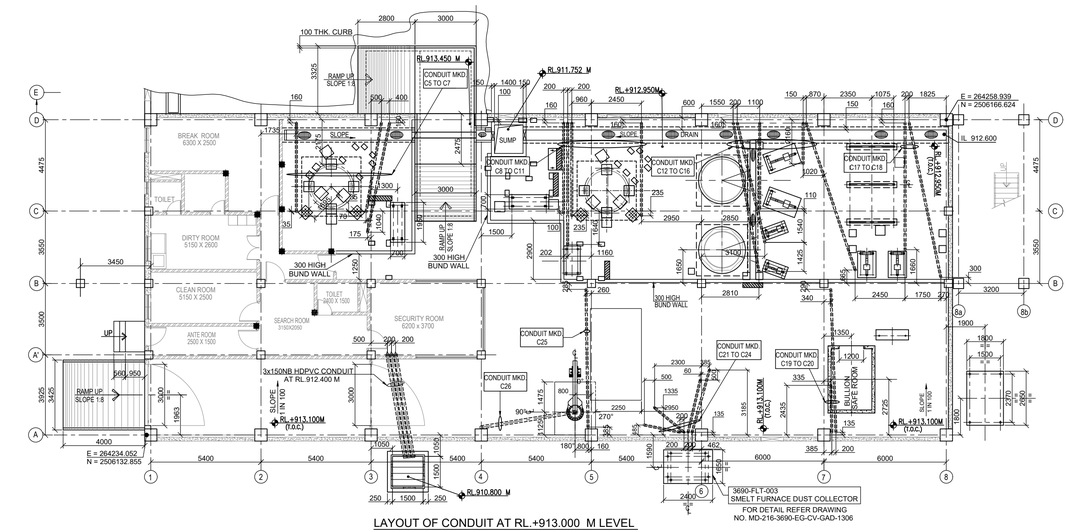


LAYOUT OF CONDUIT AT RL.+913.000 M LEVEL
SCALE 1:100

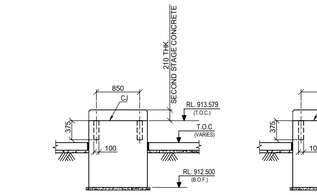


SECTION : B-B
SCALE 1:40

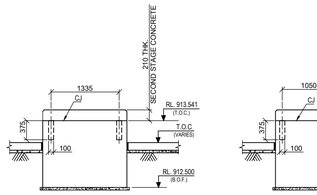


SECTION : C-C
SCALE 1:40

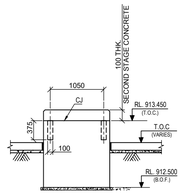


SECTION : D-D
SCALE 1:40

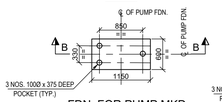


FDN. FOR PUMP MKD.
3680-PMP-003,004
SCALE 1:40

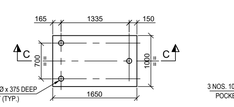


FDN. FOR PUMP MKD.
3680-PMP-005,006
SCALE 1:40

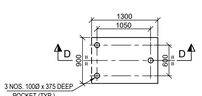


FDN. FOR PUMP MKD.
3680-PMP-001,002
SCALE 1:40

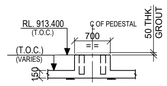

SECTION J-J
SCALE 1:40

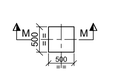

FDN. FOR PUMP MKD.
3690-PMP-001,002,003,006
SCALE 1:40

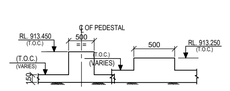

SECTION M-M
SCALE 1:40


SECTION P-P
SCALE 1:25

SECTION D1-D1
SCALE 1:40

SECTION D2-D2
SCALE 1:40

SECTION T-T
SCALE 1:25

LAYOUT OF FLOOR AT RL.+912.600 M LEVEL
(FOR POSITION OF PLATFORM SUPPORT PEDESTALS REFER DRAWING NO. MD-216-3690-EG-CV-GAD-1361)
SCALE 1:100

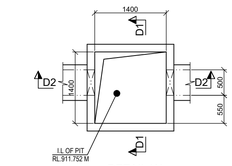

DETAIL 'A'
SCALE 1:40

SCHEDULE OF CONDUIT :-


CONDUIT MKD.	HDPVC PIPE DIA.	ELEVATION AT ℄ OF CONDUIT
C5	100Ø	RL 912.055
C6	100Ø	RL 912.055
C7	100Ø	RL 912.055
C8	100Ø	RL 912.055
C9	100Ø	RL 912.055
C10	100Ø	RL 912.055
C11	100Ø	RL 912.055
C12	100Ø	RL 912.055
C13	100Ø	RL 912.055
C14	100Ø	RL 912.055
C15	100Ø	RL 912.055
C16	100Ø	RL 912.055
C617	100Ø	RL 912.055
C618	100Ø	RL 912.055

SCHEDULE OF CONDUIT :-


CONDUIT MKD.	HDPVC PIPE DIA.	ELEVATION AT ℄ OF CONDUIT
C19	100Ø	RL 912.300
C20	100Ø	RL 912.300
C21	100Ø	RL 912.300
C22	100Ø	RL 912.300
C23	100Ø	RL 912.300
C24	100Ø	RL 912.300
C25	100Ø	RL 912.300
C26	150Ø	RL 912.300

SCHEDULE OF CONDUIT :-
(REFER DRAWING NO. NO. MD-216-3690-EG-CV-GAD-1361)


CONDUIT MKD.	HDPVC PIPE DIA.	ELEVATION AT ℄ OF CONDUIT
C1	100Ø	RL 912.275
C2	100Ø	RL 912.275
C3	100Ø	RL 912.275
C4	100Ø	RL 912.275

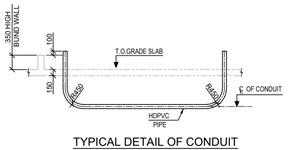

TYPICAL DETAIL OF CONDUIT
(INSIDE BUND WALL)
SCALE 1:50

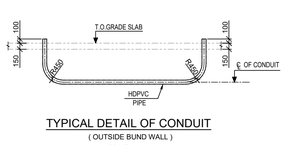

TYPICAL DETAIL OF CONDUIT
(OUTSIDE BUND WALL)
SCALE 1:50

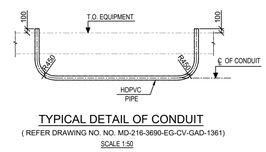

TYPICAL DETAIL OF CONDUIT
(REFER DRAWING NO. NO. MD-216-3690-EG-CV-GAD-1361)
SCALE 1:50

LEGEND :-

F.F.L - FINISHED FLOOR LEVEL
R.L - REDUCED LEVEL
P.C.C - PLAIN CEMENT CONCRETE
TYP. - TYPICAL
T.O.C - TOP OF CONCRETE
B/S - BOTH SIDE
FDN. - FOUNDATION
MKD. - MARKED

NOTES:-

1. ALL DIMENSIONS ARE IN MILLIMETRES AND LEVELS AND CO-ORDINATES ARE IN METRES UNLESS OTHERWISE STATED.
2. NET SAFE BEARING CAPACITY OF SOIL AT BOTTOM OF FOUNDATION CONSIDERED 400kN/ SQ. M
3. IF ANY PART OF FOUNDATION COMES ON BACKFILL ZONE OF ADJACENT FOUNDATION OR ANY LOOSE SOIL ARE ENCOUNTERED BELOW FOUNDATION LEVEL THE SAME SHALL BE REMOVED AND FILLED WITH PCC.
4. THE CONTENTS OF THIS DRAWING SHALL CONFORM TO THE PROVISIONS OF CIVIL, STRUCTURAL AND ARCHITECTURAL DESIGN CRITERIA DOC # MD-216-1000-EG-ST-CRT-1001
5. THIS DRAWING SHOULD BE READ WITH DRAWING NO. MD-216-3690-EG-CV-GAD-1357,1358,1359,1361 MD-216-3690-EG-CV-DED-1364,1365,1366,1367,1368

DOCUMENT NUMBER	REFERENCE DOCUMENTS	REV	DATE	REVISION DESCRIPTION	DRN	CHK	ENG	APP	EMP
		D01	20/03/2023	AS BUILD	AUD	SJM	SNM	PRI	
		C04	14/04/2021	ISSUED FOR CONSTRUCTION AND REVISED AS MARKED	AUD	SJM	SNM	PRI	
MD-216-3690-EG-ST-GAD-1002	PLAN AT +925.251, SECTION A-A, B-B AND C-C	C03	22/02/2021	ISSUED FOR CONSTRUCTION AND REVISED AS MARKED	AUD	SJM	SNM	PRI	
MD-216-3690-EG-ST-GAD-1001	PLAN AT +925.251, SECTION A-A & E-E	C02	12/12/2020	ISSUED FOR CONSTRUCTION AND REVISED AS MARKED	AUD	SJM	SNM	PRI	
MD-216-3690-EG-CV-GAD-1002	PLAN AT EL. +913.100 GOLD ROOM AND ELECTROWINNING	C01	26/06/2020	ISSUED FOR CONSTRUCTION	AUD	SJM	SNM	PRI	
MD-216-3690-EG-CV-GAD-1001	PLAN AT EL. +913.100 GOLD ROOM AND ELECTROWINNING	A01	30/05/2020	ISSUED FOR REFERENCE	AUD	SJM	SNM	PRI	

RESERVED FOR VENDOR LOGO AND DRAWING NUMBER

LARSEN & TOUBRO
This drawing is the property of LARSEN & TOUBRO and must not be passed on to any person or body not authorized by us to receive it nor be copied or otherwise made use either in full or in part by such person or body without our prior permission in writing.

Outotec
The content of these documents are the sole property of Outotec Oyj. Any rights not expressly granted herein are reserved. Reproduction, transfer or distribution of part or all of the contents in any form without prior written permission of Outotec is prohibited.

MA'ADEN معادن
Saudi Arabian Mining Company شركة معادن السعودية
This document and the information contained herein is Ma'aden proprietary know-how. This document or any part thereof should not be reproduced, stored in a retrieval system or transmitted by any means, electronic or otherwise, or divulged without prior written permission of Ma'aden.

LARSEN & TOUBRO DRAWING NUMBER	019045_450_C_G_24145_004
REVISION	5
OUTOTEC DRAWING NUMBER	900707__GAU01__EE14__MTL01__36917
DOCUMENT ID	OU100684645
REVISION	5
DRAWN	AUD 20/05/2020
CHECKED	SJM 25/05/2020
ENGINEER	SNM 10/05/2020
APPROVED	PRI 27/05/2020
EMPLOYER	
SCALE	1:100
	A0

MANSOURAH - MASSARAH GOLD PROJECT
GENERAL ARRANGEMENT DRAWING
GOLD ROOM
LAYOUT & DETAILS OF GRADE SLAB

DRAWING NUMBER: MD - 216 - 3690 - EG - CV - GAD - 1360
REV: D01