

DRAWING NUMBER: MD-216-3860-EG-CV-GAD-1001 REV: A02


LEVEL +912.350
1:50

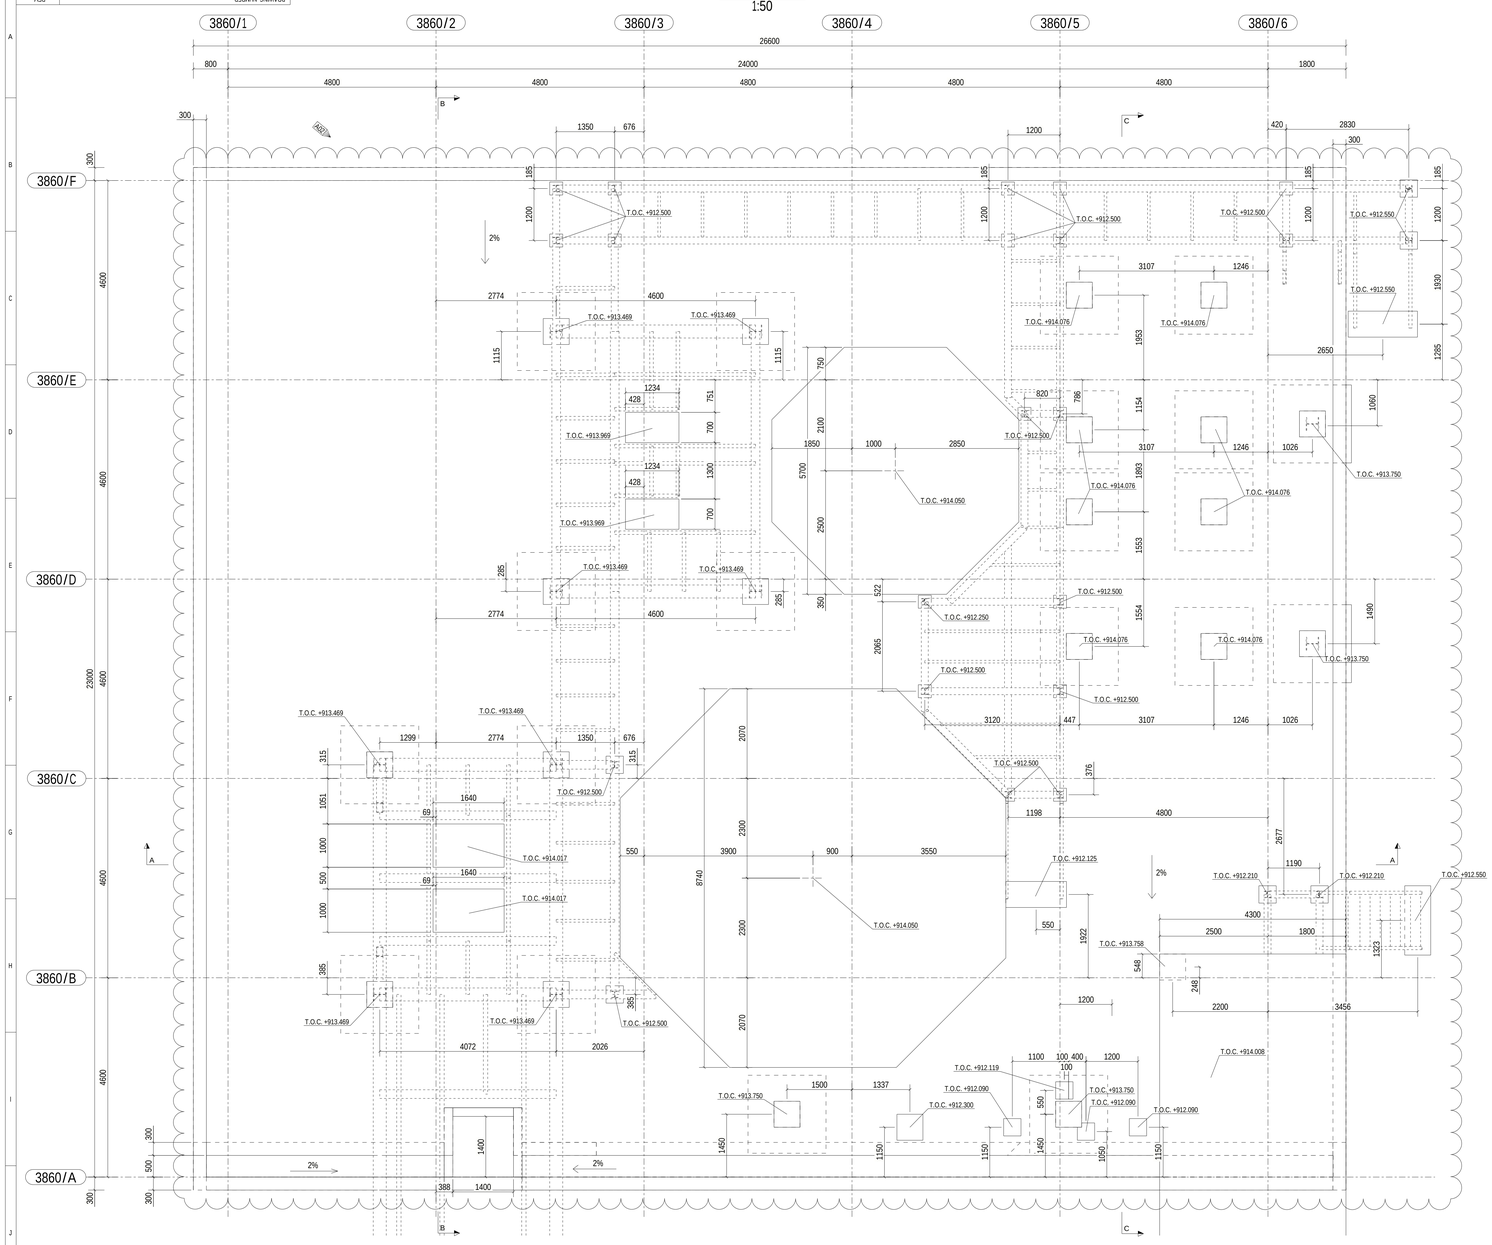


B - B
1:75

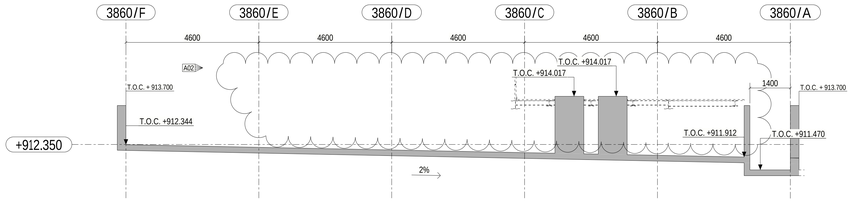

C - C
1:75

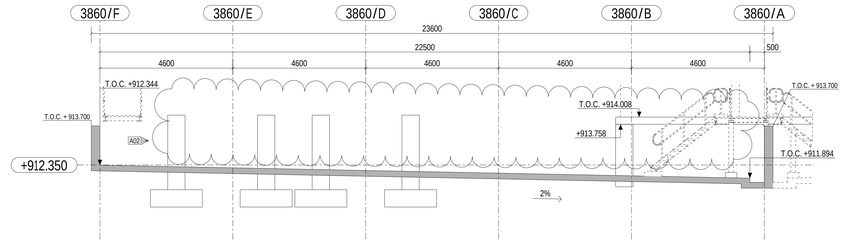

A - A
1:50

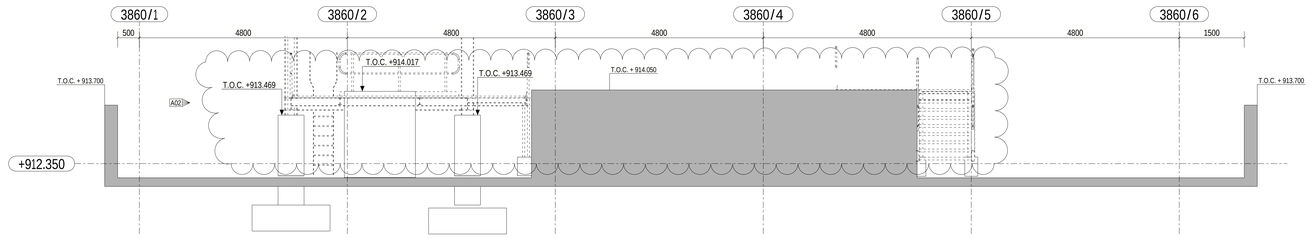


THIS DESIGN IS NOT ISSUED FOR CONSTRUCTION

FINISHED TOP GROUND LEVEL (F.G.L) FOR PROCESS AREA 3850 = RL(+)912.350 m

- CONCRETE ELEMENT FLOOR (PRE-CAST SLAB)
- CONCRETE FLOOR
- CONCRETE FLOOR WITH ACID RESISTANT COATING
- CONCRETE WALL

1. ALL DIMENSIONS ARE IN MILLIMETER, ELEVATIONS ARE IN METER UNLESS OTHERWISE STATED
2. CO-ORDINATES ARE SHOWN IN GENERAL ARRENGEMENT DRAWINGS
3. GRATING TYPE (FRP OR NORMAL) IS SPECIFIED IN GENERAL ARRENGEMENT DRAWINGS
4. F.F.L, F.G.L, T.O.C = FINISHED FLOOR LEVEL, FINISHED GROUND LEVEL, TOP OF CONCRETE, T.O.S, B.O.S, B.O.B, = TOP OF STEEL, BOTTOM OF STEEL, BOTTOM OF BASE PLATE
5. BUILDING DIMENSIONS AND HEIGHTS ARE TENTATIVE, SHALL BE FINALIZED DURING DETAIL ENGINEERING SUBJECT TO MINIMUM AS SHOWN.
6. ALL MAINTENANCE FACILITIES, HANDLING PROVISIONS, ACCESS WAYS, PLATFORMS FOR MAINTENANCE SHALL BE PROVIDED DURING DETAIL ENGINEERING WHICH ARE NOT SHOWN ENTIRELY, THIS DRAWING IS TO BE CONSIDERED AS CONCEPTUAL ARRANGEMENT OF THE FACILITIES.

KEYPLAN

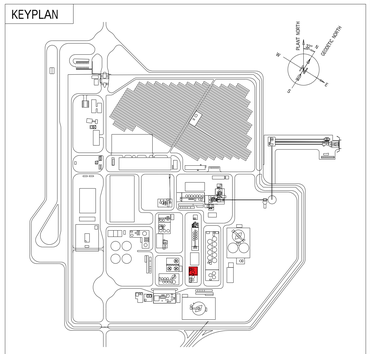

DOCUMENT NUMBER	REFERENCE DOCUMENTS	DOCUMENT NUMBER	REFERENCE DOCUMENTS
MD-216-1000-EG-ST-CRT-0001	CIVIL,STRUCTURAL AND ARCHITECTURAL DESIGN BASIS	MD-216-3860-EG-ST-GAD-1001	PLAN VIEW 3860/A-6/C-F, 3D VIEW AND SECTIONS
MD-216-3850-EG-ME-GAD-1008	SECTION B-B	MD-216-3850-EG-ME-GAD-1009	SECTION C-C
MD-216-3850-EG-ME-GAD-1006	PLAN VIEW	MD-216-3850-EG-ME-GAD-1007	SECTION A-A
MD-216-3850-EG-ME-GAD-1004	PLAN AT EL. +912.350	MD-216-3850-EG-ME-GAD-1005	PLAN AT EL. +919.990

REV	DATE	REVISION DESCRIPTION	DRN	CHK	ENG	APP	EMP
A02	24.07.2020	ISSUED FOR DETAIL DESIGN; FOUNDATIONS, SUMP AND GUTTERS MODIFIED	SebMuu	MikLai	LuiPiz	SouCha	
A01	07.02.2020	ISSUED FOR APPROVAL	KirJok	MikLai	LuiPiz	SouCha	

RESERVED FOR VENDOR LOGO AND DRAWING NUMBER

LARSEN & TOUBRO

This drawing is the property of LARSEN & TOUBRO and must not be passed on to any person or body not authorised by us to receive it nor be copied or otherwise made use either in full or in part by such person or body without our prior permission in writing.

Outotec

The content of these documents are the sole property of Outotec Oyj. Any rights not expressly granted herein are reserved. Reproduction, transfer or distribution of part or all of the contents in any form without prior written permission of Outotec is prohibited.

MA'ADEN معادن Saudi Arabian Mining Company شركة معادن العربية السعودية

This document and the information contained herein is Ma'aden proprietary know-how. This document or any part thereof should not be reproduced, stored in a retrieval system or transmitted by any means, electronic or otherwise, or divulged without prior written permission of Ma'aden.

LARSEN & TOUBRO DRAWING NUMBER — REVISION 1

OUTOTEC DRAWING NUMBER: 900707_GAU01_AA23_CTA04_38601 — DOCUMENT ID: OU100668293 — REVISION 1

DRAWN	KirJok	07.02.2020	
CHECKED	MikLai	07.02.2020	
ENGINEER	LuiPiz	07.02.2020	
APPROVED	SouCha	07.02.2020	
EMPLOYER			
SCALE	1:50	A0	

MANSOURAH - MASSARAH GOLD PROJECT
CIVIL WORKS GUIDE DRAWING
LIMESTONE
PLAN AT EL. +912.350 AND SECTIONS

DRAWING NUMBER: MD-216-3860-EG-CV-GAD-1001 — REV: A02

Tekla Structures