

DRAWING NUMBER: MD-216-3890-EG-CV-GAD-1001 | REV: A03


LEVEL +912.400
1:100

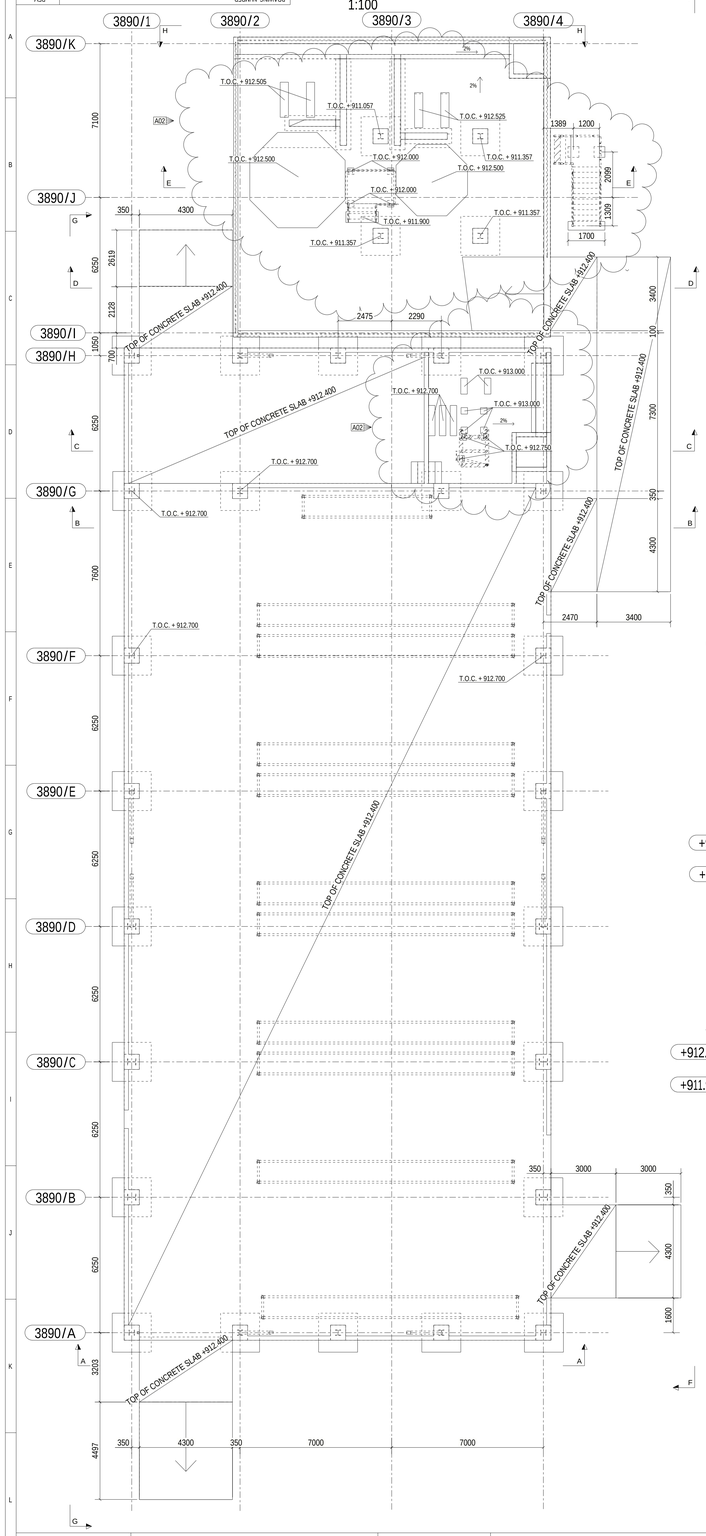


A - A
1:100

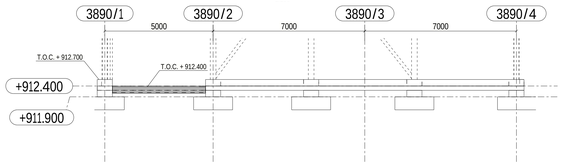


B - B
1:100

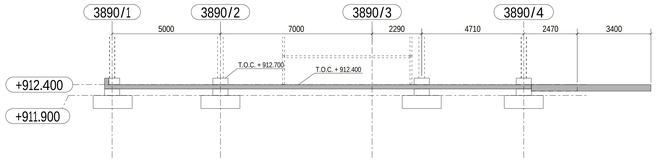


C - C
1:100

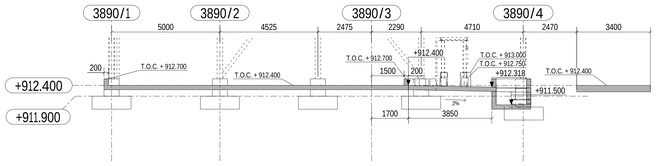


D - D
1:100

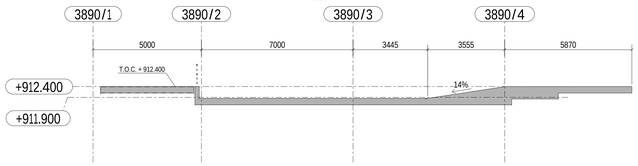

DETAIL
1:75

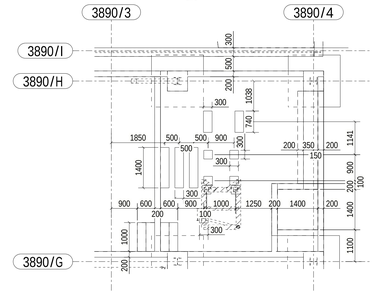

G - G
1:100

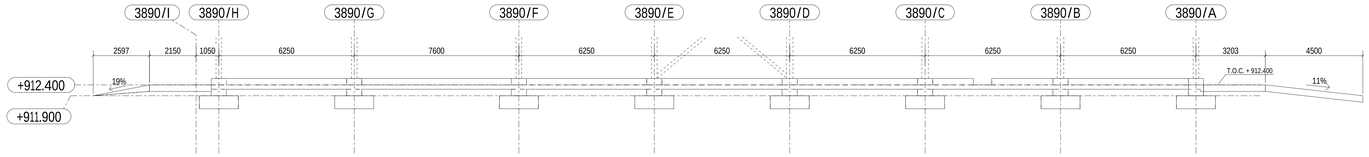


THIS DESIGN IS NOT ISSUED FOR CONSTRUCTION


FINISHED TOP GROUND LEVEL (F.G.L) FOR OUTSIDE AREA 3890 = RL(+)911.900 m

FINISHED TOP GROUND LEVEL (F.G.L) FOR INSIDE AREA 3890 = RL(+)912.400 m


F - F
1:100

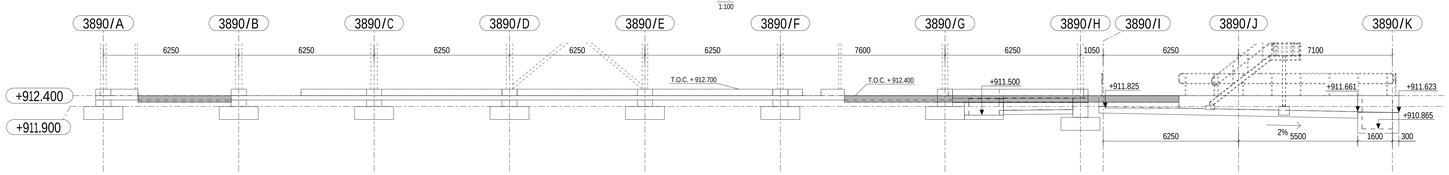


E - E
1:100

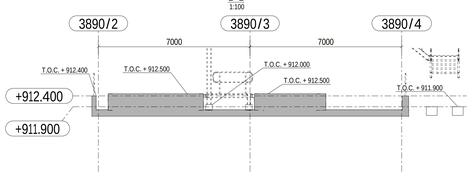

H - H
1:100

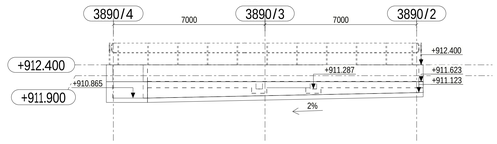


DETAIL
1:75

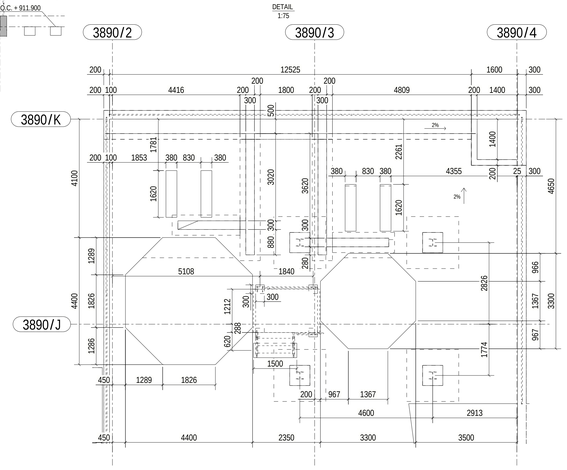

CONCRETE ELEMENT FLOOR (PRE-CAST SLAB)
CONCRETE FLOOR
CONCRETE FLOOR WITH ACID RESISTANT COATING
CONCRETE WALL

1. ALL DIMENSIONS ARE IN MILLIMETER, ELEVATIONS ARE IN METER UNLESS OTHERWISE STATED
2. CO-ORDINATES ARE SHOWN IN GENERAL ARRENGEMENT DRAWINGS
3. GRATING TYPE (FRP OR NORMAL) IS SPECIFIED IN GENERAL ARRENGEMENT DRAWINGS
4. F.F.L, F.G.L, T.O.C = FINISHED FLOOR LEVEL, FINISHED GROUND LEVEL, TOP OF CONCRETE, T.O.S, B.O.S, B.O.B, = TOP OF STEEL, BOTTOM OF STEEL, BOTTOM OF BASE PLATE
5. BUILDING DIMENSIONS AND HEIGHTS ARE TENTATIVE, SHALL BE FINALIZED DURING DETAIL ENGINEERING SUBJECT TO MINIMUM AS SHOWN.
6. ALL MAINTENANCE FACILITIES, HANDLING PROVISIONS, ACCESS WAYS, PLATFORMS FOR MAINTENANCE SHALL BE PROVIDED DURING DETAIL ENGINEERING WHICH ARE NOT SHOWN ENTIRELY. THIS DRAWING IS TO BE CONSIDERED AS CONCEPTUAL ARRANGEMENT OF THE FACILITIES.

KEYPLAN

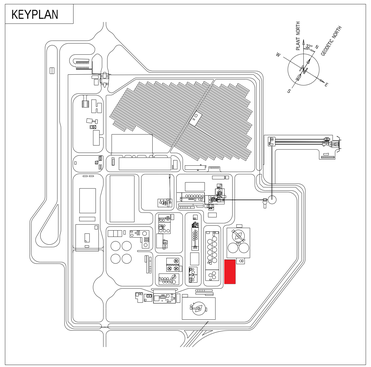

Document Number
MD-216-3890-EG-CV-GAD-1001

Revision A03

Approved

Mr Doron Golan - Bechtel Global
Jun 28, 2021, 5:41 PM GMT-4:00

Permission to proceed does not constitute acceptance or approval of design detail, calculations, analysis, test methods, or materials developed or selected by the Supplier, and does not relieve the Supplier from full compliance with contractual obligations

DOCUMENT NUMBER	REFERENCE DOCUMENTS	DOCUMENT NUMBER	REFERENCE DOCUMENTS
MD-216-3890-EG-ST-GAD-1002	PLAN AND SECTIONS		
MD-216-1000-EG-ST-CRT-0001	CIVIL,STRUCTURAL AND ARCHITECTURAL DESIGN BASIS	MD-216-3890-EG-ST-GAD-1001	3D VIEW
MD-216-3890-EG-ME-GAD-1001	PLAN VIEW	MD-216-3890-EG-ME-GAD-1002	SECTION A-A, B-B & C-C

REV	DATE	REVISION DESCRIPTION	DRN	CHK	ENG	APP	EMP
A03	01.06.2021	ISSUED FOR DETAIL DESGN	NikSm	MikLai	LuiPiz	SuoCha	
A02	10.07.2020	Issued for approval (area was rotated/concrete fundations modified/added)	NikSm	MikLai	LuiPiz	SuoCha	
A01	17.01.2020	ISSUED FOR APPROVAL	KirJok	MikLai	LuiPiz	SuoCha	

REV	DATE	REVISION DESCRIPTION	DRN	CHK	ENG	APP	EMP

RESERVED FOR VENDOR LOGO AND DRAWING NUMBER

LARSEN & TOUBRO

This drawing is the property of LARSEN & TOUBRO and must not be passed on to any person or body not authorized by us to receive it nor be copied or otherwise made use either in full or in part by such person or body without our prior permission in writing.

Outotec

The content of these documents are the sole property of Outotec Oy. Any rights not expressly granted herein are reserved. Reproduction, transfer or distribution of part or all of the contents in any form without prior written permission of Outotec is prohibited.

MA'ADEN معادن
Saudi Arabian Mining Company شركة معادن العربية السعودية

This document and the information contained herein is Ma'aden proprietary know-how. This document or any part thereof should not be reproduced, stored in a retrieval system or transmitted by any means, electronic or otherwise, or divulged without prior written permission of Ma'aden.

L'ARSEN & TOUBRO DRAWING NUMBER | REVISION 2

OUTOTEC DRAWING NUMBER: 900707_GAU01_AA04_CTA04_38901 | DOCUMENT ID: OU100668170 | REVISION 2

DRAWN	KirJok	17.01.2020
CHECKED	MikLai	17.01.2020
ENGINEER	LuiPiz	17.01.2020
APPROVED	SuoCha	17.01.2020
EMPLOYER		
SCALE	1:100	A0

MANSOURAH - MASSARAH GOLD PROJECT
CIVIL WORKS GUIDE DRAWING
SMBS AND PEROXIDE
PLAN AT EL. +912.400 AND +911.900

DRAWING NUMBER: MD-216-3890-EG-CV-GAD-1001 | REV: A03

Trella Structures