


DRAWING NUMBER: MD - 216 - 49PR - EG - CV - GAD - 2013
REV: D01

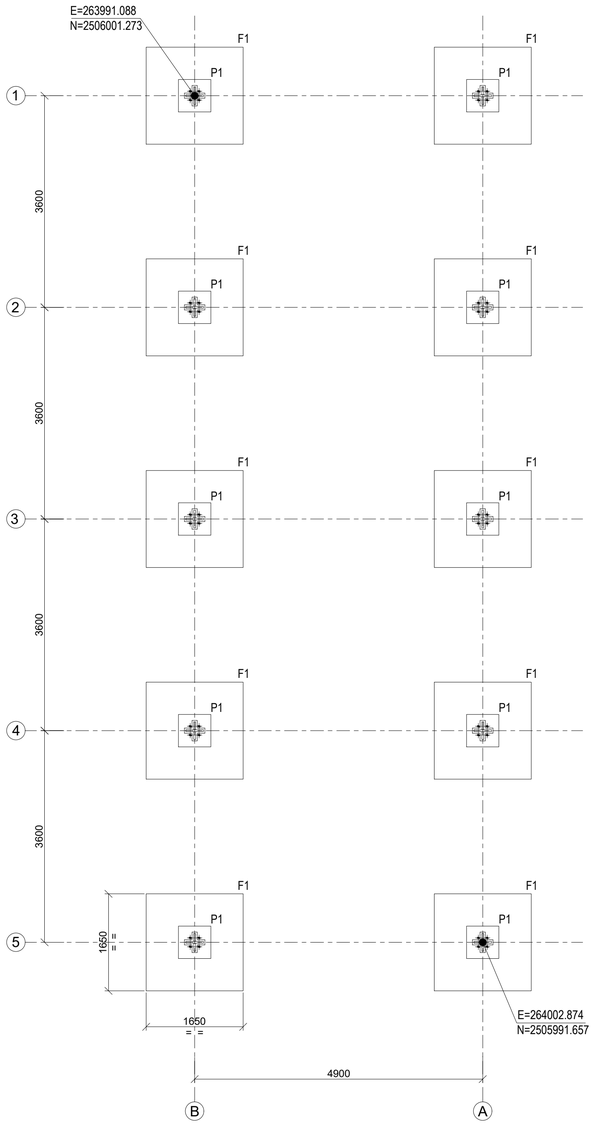


LAYOUT OF FOUNDATION
(SCALE 1:50)

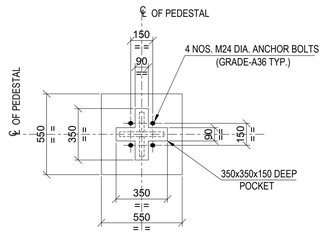


VIEW B - B
(TYP. DETAIL OF PEDESTAL MKD. P1)
(SCALE- 1:20)

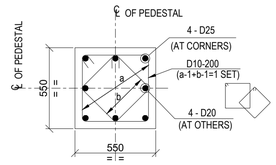


RC DETAIL OF PEDESTAL MKD. P1
(SCALE- 1:20)

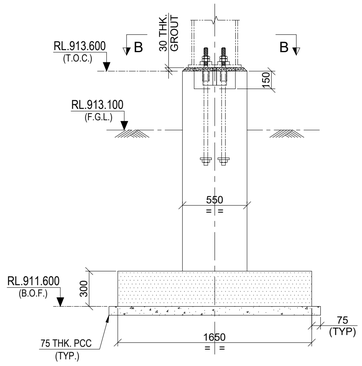


SECTION A-A
(SCALE - 1:25)

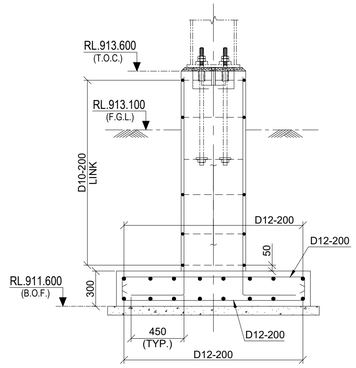


SECTION 1-1
(SCALE - 1:25)

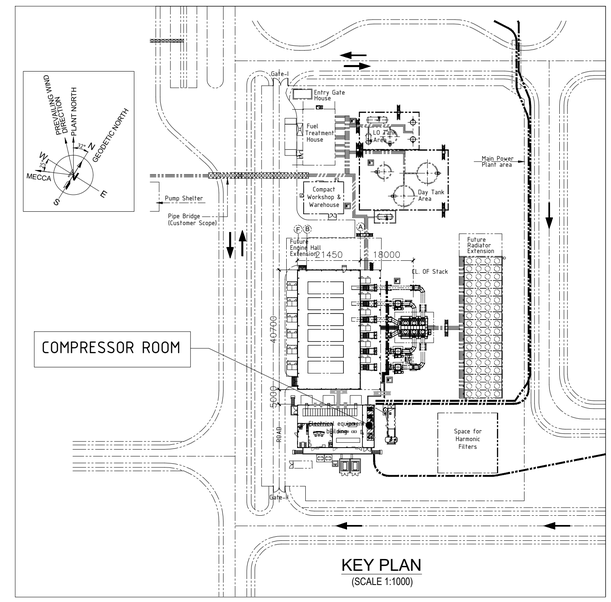

KEY PLAN
(SCALE 1:1000)

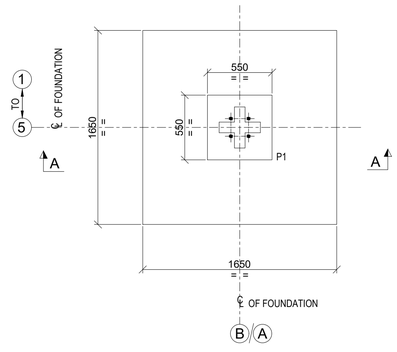

DETAIL OF FOUNDATION MKD. F1
(SCALE - 1:25)

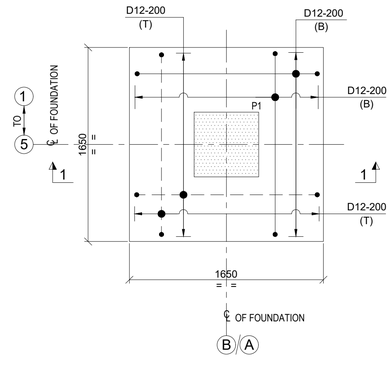

R.C. DETAIL OF FOUNDATION MKD. F1
(10 NOS. REQUIRED)
(SCALE - 1:25)

SCHEDULE OF BOLTS

BOLT DIA. (MM)	BOLT NUMBERS REQUIRED
M24	40

LEGEND :-

RL. - REDUCED LEVEL.
T.O.C. - TOP OF CONCRETE.
F.G.L. - FINISHED GROUND LEVEL.
B.O.F. - BOTTOM OF FOOTING.
CL - CENTRE LINE.
TYP. - TYPICAL.
THK. - THICK.
MKD. - MARKED.
G.A. - GENERAL ARRANGEMENT.
DIA - DIAMETER.

NOTES :-

1. ALL DIMENSIONS ARE IN MILLIMETERS AND LEVELS AND CO-ORDINATES ARE IN METERS. UNLESS OTHERWISE STATED.
2. GRADE OF CONCRETE SHALL BE 35 MPa FOR FOUNDATION & 15 MPa FOR BLINDING CONCRETE.
3. GRADE OF REINFORCEMENT SHALL BE DEFORMED BAR 420 MPa (GRADE 60) - ASTM A615/A615M.
4. NET SAFE BEARING CAPACITY OF SOIL AT BOTTOM OF FOUNDATION CONSIDER 500KN/ SQ. M.
5. CLEAR COVER TO MAIN REINFORCEMENT SHALL BE 75 mm FOR RAFT & 50 mm FOR COLUMN.
6. IF ANY PART OF FOUNDATION COMES ON BACKFILL ZONE OF ADJACENT FOUNDATION OR ANY LOOSE SOIL ARE ENCOUNTERED BELOW FOUNDATION LEVEL THE SAME SHALL BE REMOVED AND FILLED WITH PCC.
7. ALL OTHER NOTES REFER DRAWING NO. MD-101-SMEM-EG-ST-DST-0001 TO 0008.
8. GENERAL NOTES FOR CIVIL WORKS & STANDARD REINFORCEMENT DETAIL REFER DRAWING NO. MD-216-1000-EG-CV-DED-1001 & 1005.
9. FOR ANCHOR BOLTS STANDARD DETAILS. REFER DRAWING NO. MD-216-1000-EG-CV-DED-1003

DOCUMENT NUMBER	REFERENCE DOCUMENTS			REVISION DESCRIPTION	DRN	CHK	ENG	APP	EMP
MD-216-49PR-EG-ST-GAD-2001	COMPRESSOR ROOM PLAN, ELEVATIONS, SECTIONS & DETAILS	D01	30/03/2023	AS - BUILT	PDK	SGC	SHD	PRI	
MD-216-49PR-EG-ME-GAD-1111	POWER GENERATION COMPRESSOR ROOM	C02	24/11/2020	ISSUED FOR CONSTRUCTION & REVISED AS MKD. C02	PDK	SGC	SHD	PRI	
MD-216-49PR-EG-ME-LAD-V553-1002	LAYOUT OF POWER GENERATION	C01	31/08/2020	ISSUED FOR CONSTRUCTION	AMJ	SGC	SHD	PRI	
MD-216-1000-EG-ST-CRT-1001	CIVIL,STRUCTURAL AND ARCHITECTURAL DESIGN CRITERIA	A01	31/07/2020	ISSUED FOR REFERENCE	AMJ	SGC	SHD	PRI	

RESERVED FOR VENDOR LOGO AND DRAWING NUMBER

LARSEN & TOUBRO
This drawing is the property of *LARSEN & TOUBRO* and must not be passed on to any person or body not authorized by us to receive it nor be copied or otherwise made use either in full or in part by such person or body without our prior permission in writing.

Outotec
The content of these documents are the sole property of Outotec Oyj. Any rights not expressly granted herein are reserved. Reproduction, transfer or distribution of part or all of the contents in any form without prior written permission of Outotec is prohibited.

MA'ADEN معادن
Saudi Arabian Mining Company شركة التعدين العربية السعودية
This document and the information contained herein is Ma'aden proprietary know-how. This document or any part thereof should not be reproduced, stored in a retrieval system or transmitted by any means, electronic or otherwise, or divulged without prior written permission of Ma'aden.

LARSEN & TOUBRO DRAWING NUMBER	O19045_008_C_G_24292_007	REVISION 3
OUTOTEC DRAWING NUMBER	900707 _GAU01 _WG01_MTL01 _45083	DOCUMENT ID OU100688141 / REVISION 3

DRAWN	AMJ	29/07/2020
CHECKED	SGC	30/07/2020
ENGINEER	SHD	28/07/2020
APPROVED	PRI	31/07/2020
EMPLOYER		
SCALE	1:75, 1:25 & 1:15	A1

MANSOURAH - MASSARAH GOLD PROJECT
GENERAL ARRANGEMENT
POWER PLANT COMPRESSOR ROOM
GA AND DETAIL OF FOUNDATION

DRAWING NUMBER: MD - 216 - 49PR- EG - CV - GAD - 2013
REV: D01